
KiCad Design Rules Check

0 errors, 0 unconnected items, and 4 mounting-hole courtyard warnings.

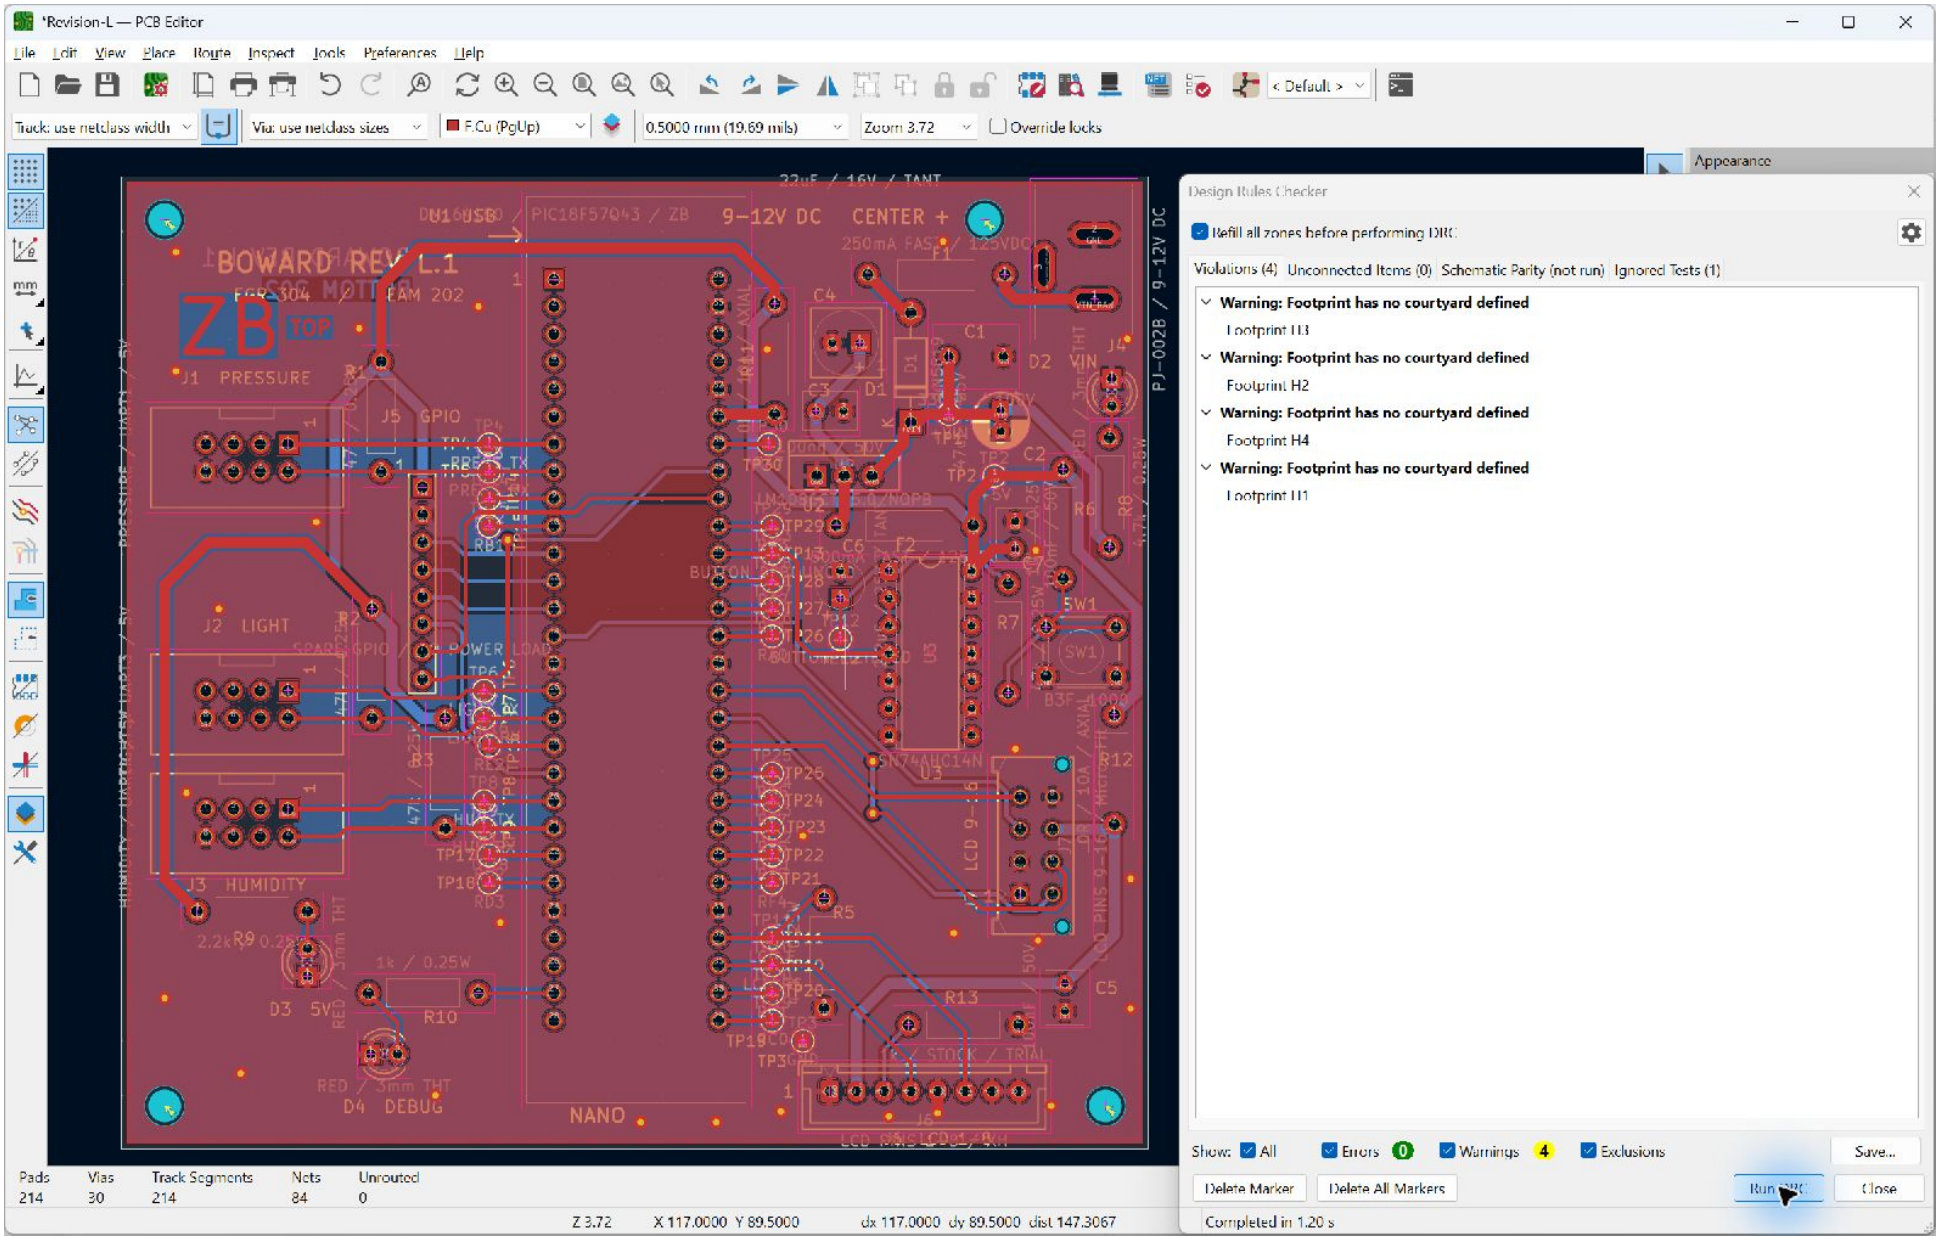

The separate KiCad CLI report found 0 schematic mismatches.

Board and results in the same frame.